
宁波协诚集团样品展厅 · 方案 A · 第 2 版

中央环岛 · 环游叙事 · 概念方案（非施工图） · 2026-11-10 · 场地 26.17 × 17.92 m / 层高 3.0 m

> **一句话：7.0 × 4.8 m 的中岛不再是一只方盒子——三级圆角台层层收进，头顶 R2400 环形灯槽与它同形；北墙的展墙翼斜 12° 让光漏进来，入口的胡桃木品牌墙弯成一道弧，把视线推到中岛。**

现代轻奢 | 暖白橡木 + 哑光铜 | 微水泥地面 | 2700–3000K | 低饱和米金

① 两张图

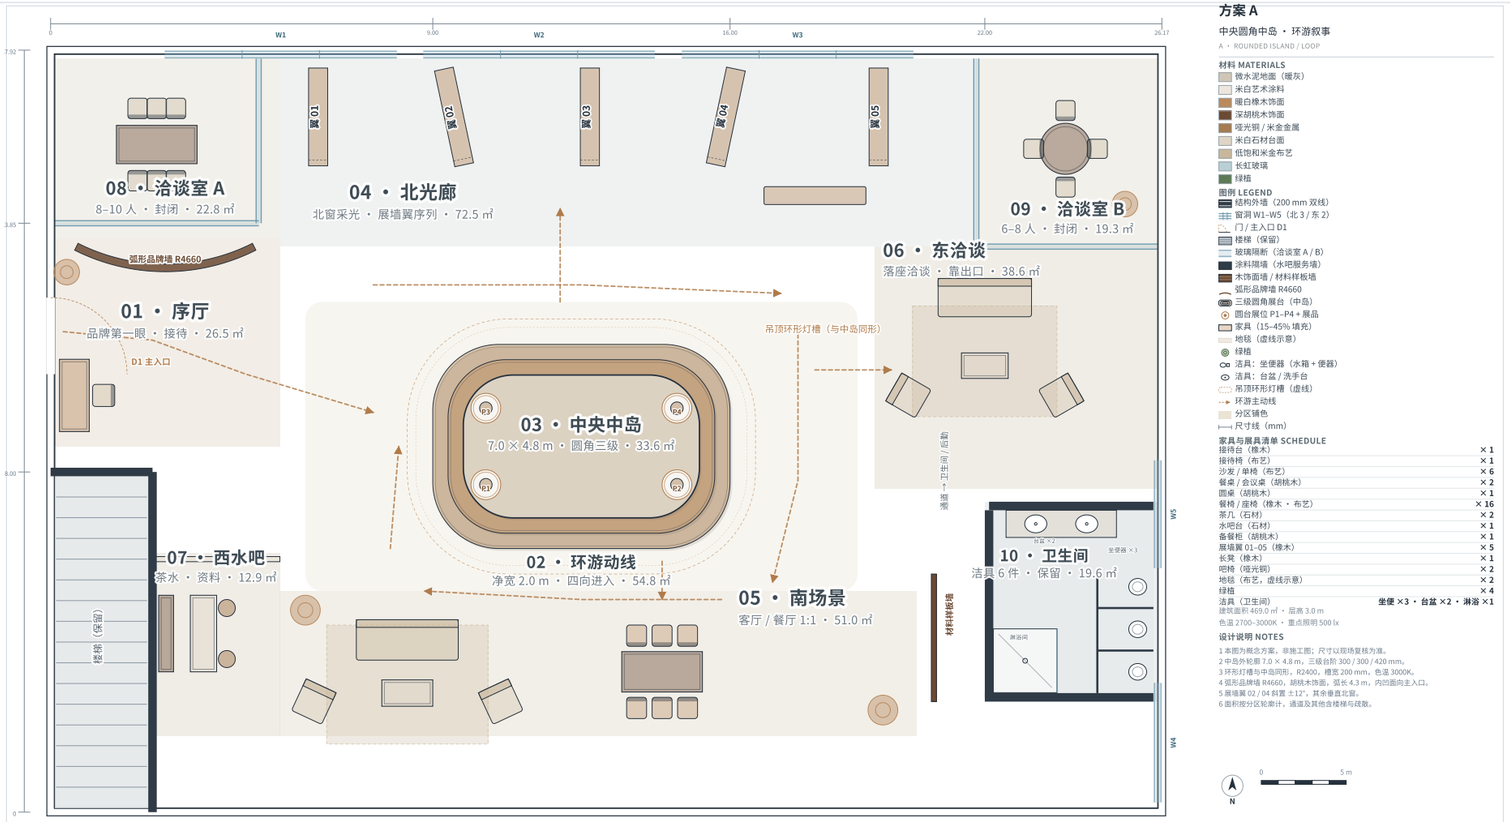

宁波协诚集团样品展厅 · 方案 A 平面布置图

CONCEPT FLOOR PLAN · SCALE 1:100 · 概念方案（非施工图）

建筑面积 469.0 ㎡ · 层高 3.0 m · 图纸 A-02 · 2026-11-10

本图与效果图由同一份设计数据（方案A_设计数据.json）生成；尺寸以现场复核为准

圆角中岛 R1560 / R1360 / R1180 · 弧形品牌墙 R4660 · 展墙翼 02 / 04 斜置 ±12°

方案 A

中央圆角中岛 · 环游叙事

A · ROUNDED ISLAND / LOOP

材料 MATERIALS

- 微水泥地面（暖灰）
- 米白艺术涂料
- 暖白橡木饰面
- 深胡桃木饰面
- 哑光铜 / 米金金属
- 米白石材台面
- 低饱和米金布艺
- 长虹玻璃
- 绿植

图例 LEGEND

- 结构外墙（200 mm 双线）
- 窗洞 W1–W5（北 3 / 东 2）
- 门 / 主入口 D1
- 楼梯（保留）
- 玻璃隔断（洽谈室 A / B）
- 涂料隔墙（水吧服务墙）
- 木饰面墙 / 材料样板墙
- 弧形品牌墙 R4660
- 三级圆角展台（中岛）
- 圆台展位 P1–P4 + 展品
- 家具（15–45% 填充）
- 地毯（虚线示意）
- 绿植
- 洁具：坐便器（水箱 + 便器）
- 洁具：台盆 / 洗手台
- 吊顶环形灯槽（虚线）
- 环游主动线
- 分区铺色
- 尺寸线（mm）

家具与展具清单 SCHEDULE

接待台（橡木）	× 1
接待椅（布艺）	× 1
沙发 / 单椅（布艺）	× 6
餐桌 / 会议桌（胡桃木）	× 2
圆桌（胡桃木）	× 1
餐椅 / 座椅（橡木 · 布艺）	× 16
茶几（石材）	× 2
水吧台（石材）	× 1
备餐柜（胡桃木）	× 1
展墙翼 01–05（橡木）	× 5
长凳（橡木）	× 1
吧椅（哑光铜）	× 2
地毯（布艺，虚线示意）	× 2
绿植	× 4
洁具（卫生间）	坐便 ×3 · 台盆 ×2 · 淋浴 ×1

建筑面积 469.0 ㎡ · 层高 3.0 m

色温 2700–3000K · 重点照明 500 lx

设计说明 NOTES

1 本图为概念方案，非施工图；尺寸以现场复核为准。
2 中岛外轮廓 7.0 × 4.8 m，三级台阶 300 / 300 / 420 mm。
3 环形灯槽与中岛同形，R2400，槽宽 200 mm，色温 3000K。
4 弧形品牌墙 R4660，胡桃木饰面，弧长 4.3 m，内凹面向主入口。
5 展墙翼 02 / 04 斜置 ±12°，其余垂直北窗。
6 面积按分区轮廓计，通道及其他含楼梯与疏散。

N

0 5 m

面积表 AREA SCHEDULE（㎡）

编号	分区	面积
01	序厅	26.5
02	环游动线	54.8
03	中央中岛	33.6
04	北光廊	72.5
05	南场景	51.0
06	东洽谈	38.6
07	西水吧	12.9
08	洽谈室 A	22.8
09	洽谈室 B	19.3
10	卫生间	19.6
—	**通道及其他**	**117.4**
合计		**469.0 ㎡**

「通道及其他」含楼梯 19.2 ㎡、环廊、疏散通道与结构边带；不含墙体厚度

方案 A 平面布置图 1:100 · 图元全部有名称 · 含 18 项图例、家具清单、6 条设计说明、面积表（合计 469.0 ㎡）



效果图 01 · 从入口（西侧）看向中央中岛 · Blender 4.2.9 Cycles 路径追踪，1400 × 880，128 采样，7 分 04 秒 · 与平面图共用同一份 方案A_设计数据.json

② 你上一轮的四条意见，逐条对在哪

你的意见	这一版怎么改的	在图上哪里看
一、中岛不要方方正正，要和头顶发光环呼应；整套里再加 ≥2 处非直角；不要“堆叠方块”	中岛外轮廓仍是 7.0 × 4.8 m，但改成三级圆角台：R1560 → R1360 → R1180，逐级内收 360 mm、抬高 180 / 420 / 720 mm，顶层 5.56 × 3.36 m。头顶灯槽用 R2400 圆角环，同形不同尺寸。全场另有 3 处非直角：入口 R2600 弧形品牌墙（凹面正对入口）、展墙翼 02 与 04 各斜 12°。	平面图中岛（三层不同深度填色 + 每层投影）、吊顶发光环、西北角弧形品牌墙、北光廊第 2 / 4 道翼
二、平面图整理：① 每个图元要有名称，说明不了的黑线删掉 ② 区域名和面积放大、不压家具 ③ 卫生间画洁具 ④ 面积表加“通道及其他”凑满 469 ㎡	① 全图 6 道墙、45 件家具、4 个展台、7 件洁具、5 组窗，全部进图例（18 项）或家具清单（按编号可查），没有一条无名线；原来那些说不清的斜线、虚线已删除。② 区域名 360–440 pt、带白色描边光晕，全部挪到空地中央，加一行小字说明（例“展墙翼 5 道 · 光廊 2.0 m”）。③ 卫生间重画：3 组坐便器（水箱 + 内外椭圆 + 隔断）、台盆 ×2、淋浴间 1.5 × 1.5 m，共 6 件，与图上「洁具 6 件」一致。④ 面积表 10 个分区 + 通道及其他 117.4，合计正好 469.0 ㎡。	平面图四周的图例 / 家具清单 / 面积表；每个色块中央的大字

你的意见	这一版怎么改的	在图上哪里看
三、效果图没有材质、没有家具和展品、像白模——走路线 A：免安装 Blender 放进项目工具目录	Blender 4.2.9 LTS 免安装版已下载到 `tools/blender/`（386.9 MB，未装进系统，直接解压即用）。场景由 `方案A_设计数据.json` 程序化生成：微水泥 / 橡木 / 胡桃木 / 石材 / 布艺 / 铜 / 长虹玻璃共 7 类程序化材质（木纹用 Wave + 噪声扰动，石材用两层噪声 + 凹凸），3 段北窗做发光天空板 + 太阳光，室内 4 组筒灯 + 轨道射灯 + 灯槽发光环 + 铜质吊灯，45 件家具、4 组展品（车削陶瓶、立石、铜钵、叠放布样）、绿植。相机 1.50 m 人眼高度，30 mm 广角，从入口看向中岛。	效果图：地面微水泥、中岛木纹与石台面、北侧窗光与斜翼投影、头顶发光环、展台上的展品
四、验收标准：要像设计公司给客户的效果图；达不到就如实说	见第 ⑥ 节。这一版比上一版有本质变化（真材质、真光影、有家具展品），但**仍然达不到设计公司交付级**，差距写在第 ⑥ 节，没有藏。	第 ⑥ 节

③ 设计说明

空间组织（七步叙事）

- 01 序厅：入口先撞见 R2600 的弧形品牌墙，胡桃木曲线把人的视线往中岛方向带，接待台在左。
- 02 环游：中岛四周 2.0 m 环形动线，四个方向都能进，不走回头路。
- 03 中岛：外轮廓 7.0 × 4.8 m 不变，改成 R1560 / R1360 / R1180 三级圆角台，与头顶环形灯槽同形。
- 04 北光廊：北墙 3 段 5.4 m 窗带，5 道 2.3 m 展墙翼，其中 2 道 ±12° 斜置，让光从缝里洗进来。
- 05 南场景：客厅 + 餐厅两个 1:1 生活场景，材料与家具可触摸。
- 06 东洽谈：靠东墙落座区，紧邻卫生间与出口。
- 07 西水吧：楼梯旁服务点，接待、茶水、资料发放合一。

非直角元素清单

- 中央中岛：三级圆角台 R1560 / R1360 / R1180
- 吊顶环形灯槽：R2400 圆角环，与中岛同形呼应
- 弧形品牌墙：R2600 圆弧，凹面正对入口
- 展墙翼 02 / 04：±12° 斜置

与场地条件的关系

- **保留**：外墙、北向 3 段窗带、东墙 2 段窗、西南楼梯（2.4 × 8.0 m）、东南卫生间（4.17 × 4.7 m）。
- **未发现结构柱**，中岛可放场地正中，不受柱网限制。
- **拆改**：原奥创设计的 U 形展台墙、六边形展台全部取消；两间洽谈室沿用原隔墙位置，改为玻璃隔断。
- **入口**：西门厅进入先看到 R2600 弧形胡桃木品牌墙，视线顺着弧面转向中岛。

④ 面积与分区（合计 469.0 ㎡）

编号	区域	面积（㎡）
01	序厅	26.5
02	环游动线（环形）	54.8
03	中央中岛	33.6
04	北光廊	72.5
05	南场景	51.0
06	东洽谈	38.6
07	西水吧	12.9
08	洽谈室 A	22.8
09	洽谈室 B	19.3

材料	用在哪
微水泥地面（暖灰）	地面
米白艺术涂料	墙面 / 天花
暖白橡木饰面	中岛台体、展墙翼、家具
深胡桃木饰面	弧形品牌墙、接待台背板
哑光铜 / 米金金属	灯具、五金、展品底座
米白石材台面	中岛顶层台面
低饱和米金布艺	沙发、单椅、窗帘
长虹玻璃	洽谈室隔断
绿植	光廊与场景角落

编号	区域		面积（㎡）
10	卫生间	19.6	
—	通道及其他	117.4	
—	**合计**		**469.0**
—	场地外包尺寸 26.17 × 17.92		469.0（含墙体）

材料表与效果图、平面图出自同一份 JSON，改一处三处同步。

⑤ 灯光

部位	做法	色温 / 照度
中岛发光环	吊顶 R2400 圆角环形灯槽，槽内藏灯带向下洗石材台面	2700K，台面 500 lx
北光廊	轨道射灯 4 只 25° 洗展墙翼；斜置翼 02 / 04 让光从缝里漏到地面	3000K，墙面 300 lx
场景区	餐桌双吊灯（铜质灯罩），距桌面 750 mm；客厅落地灯	2700K，桌面 200 lx
基础照明	3 条东西向线性灯槽 + 窗侧日光，白天可只开 30%	3000K，环境 150 lx
洽谈室	每间 2 只筒灯 + 桌面台灯，玻璃隔断保持通透	3000K，桌面 300 lx

⑥ 这一版做到哪、没做到哪（如实）

做到了：材质不再是灰白体块——木纹、石材、微水泥、布艺、铜、玻璃在渲染里都能分辨；有窗光斜投影、有灯槽溢光、有软阴影；有 45 件家具、4 组展品、绿植；相机在人眼高度；平面图与效果图由同一份数据生成，不会各说各话。

仍然不像设计公司成果的地方（我自己的判断，不是等你挑）：

- **模型是体块级，不是家具级**：沙发是圆角方块加靠背，椅子是壳 + 四条腿，展墙翼是平板。真实效果图里沙发的坐垫塌陷、缝线、木饰面的拼缝、石材的对纹，这里一样都没有。近处的家具一看就是“几何体”。
- **全部是程序化材质，没有一张贴图**：木纹是波形 + 噪声算出来的，走近看会重复、会“塑料”；石材没有真实纹理和拼缝；微水泥没有批刀痕。真实项目用的是扫描贴图（PBR）。
- **石材台面像抹灰**：中岛顶层 300 mm 石材台面没有纹理走向、没有拼缝，边缘倒圆过软，远看像一整块石膏或泡沫板。
- **展台像水泥墩**：四个展台是圆柱 + 车削体，近处的立石、铜钵、布样都只是几何体，撑不起“样品展厅”的说服力；北墙那道木饰面展墙在画面里读成了一扇木门。
- **画面左侧三分之一偏暗、偏空**：入口区只有弧形墙与接待台，玻璃隔断在暗部只读成一圈黑框，缺一个近景层次（台面上的物件、地面导向、人的尺度参照）。
- **没有反射**：微水泥地面近乎全哑，看不到家具和窗的倒影；玻璃隔断也没有反射与折射层次。
- **没有人物、没有软装细节**：书、器皿、挂画、地毯纹理、窗帘褶皱都缺。设计公司的效果图里，这些“非结构物”占了画面的可信度一大半。
- **只有 1 张图、1 个视角**：设计公司交付至少 3–5 个角度（入口、中岛近景、洽谈区、场景区、俯视），且互相能对上。

结论：这一版是“可信的空间研究图”，不是“客户交付级效果图”。按你的标准，**我不把它算通过**。要继续往上，最短的路是：① 用真实 PBR 贴图替换程序化材质；② 家具换成带细节的模型（自建或开源模型库）；③ 补天光 + 环境光遮蔽，压掉暗盘；④ 加人物与软装。这需要你点头我才往下做。

⑦ 等你决定

1. **中岛形态**：三级圆角 + R2400 灯槽这个方向对不对？要不要更“薄”（顶层再薄 60 mm）或更“厚”（加一圈铜边）。

2. **两处斜翼 12°**：斜度够不够？现在是 12°，可以到 20° 但会占掉光廊 0.3 m 净宽。
3. **效果图往哪条路走**：A 继续在 Blender 里加真实贴图 + 精修家具（不外发任何项目文件）；B 用图像通道在本地白模截图上增强（需要 `RKD_IMAGE_API_KEY`，且只发白模截图与文字提示词）。你定，我不自己选。

⑧ 文件

02_方案A_平面布置图.svg 1:100 平面布置图（第 2 版），浏览器直接打开，可放大到看清每个图元名称

03_方案A_效果图_01.png 1400 × 880，Blender Cycles 110 采样，入口看向中岛

方案A_设计数据.json 平面图与 3D 共用的一份数据（分区、墙、家具、展台、洁具、材料、灯）

阶段2_方案A.pdf 本页导出的 PDF，可直接发客户

01_真实场地底图.svg 阶段 1 底图（已确认通过，本版未改）

阶段1_底图核对.pdf 阶段 1 核对页

方案 A 第 2 版到此为止，停下等你确认。设计与效果是否成立只由你评价，本页不自评通过。管理配套（PG / NAS / 账号 / 岗位审查 / 备份恢复）本阶段全部冻结。渲染图未经过任何外部图像模型，全部本机 Blender 直出，本轮外发图片 0 张、费用 0。